



СТЕНД РК-200. СХЕМА ЭЛЕКТРИЧЕСКАЯ ПРИНЦИПИАЛЬНАЯ

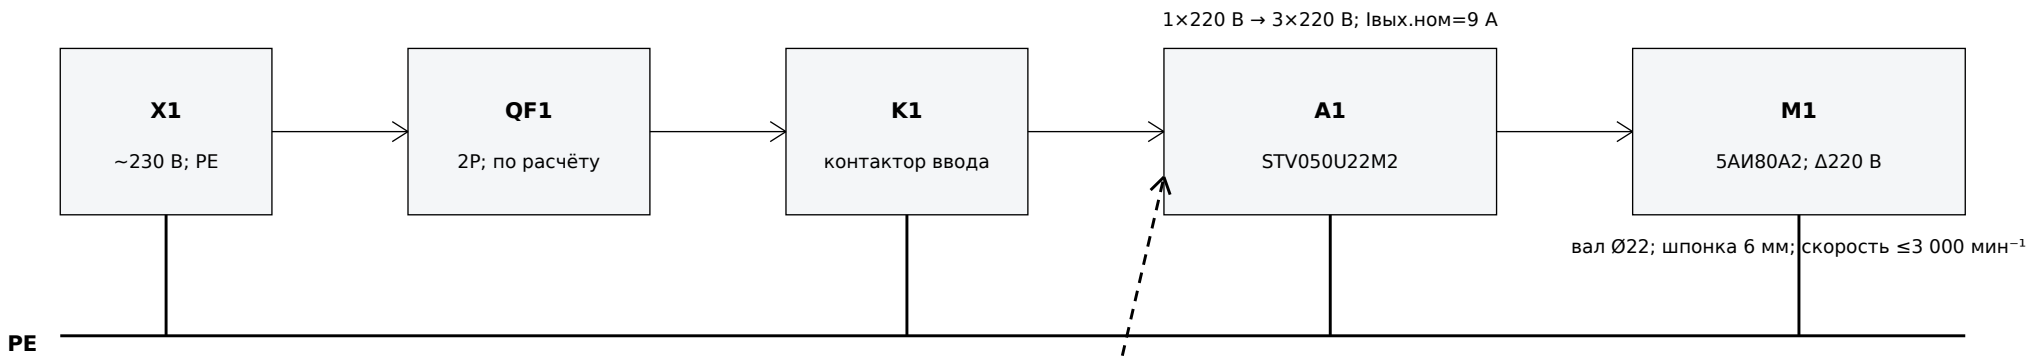

ЦЕПЬ РАЗРЕШЕНИЯ И АВАРИЙНОГО ОСТАНОВА, 24 В DC

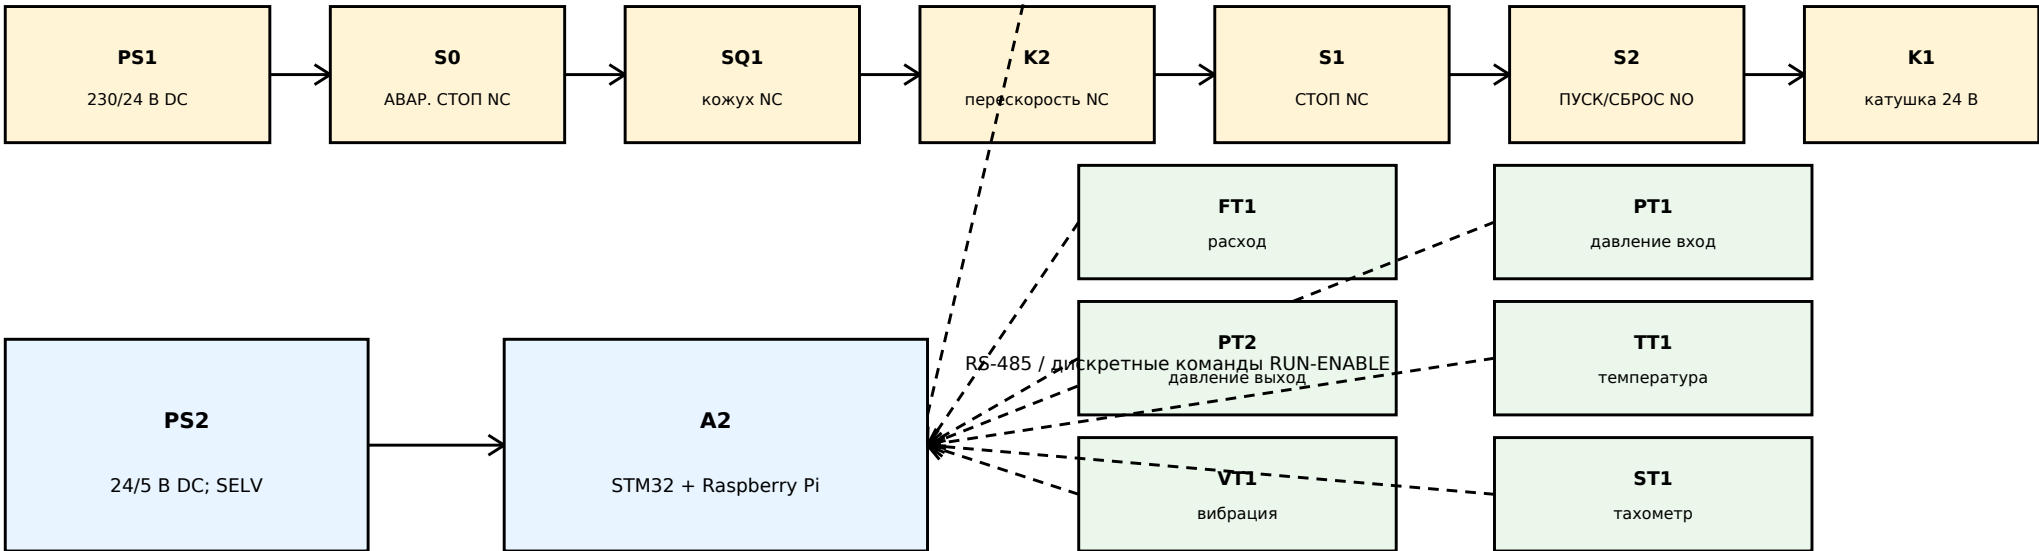

ПРИМЕЧАНИЯ

1. QF1, K1, кабели и клеммы назначить расчётом и по руководству STV050.
2. Перед подключением подтвердить шильдик двигателя Δ220/У380 В.
3. Нормальный останов выполняет ПЧ; K1 служит цепью разрешения/аварийного снятия питания.
4. Коммутация U-V-W при работающем или заряженном ПЧ запрещена.
5. Максимальная скорость 3 000 мин⁻¹ контролируется ST1 и независимым K2.
6. Пуск разрешён только при закрытом защитном корпусе и исправном аварийном останове.
7. Точка 12 000 мин⁻¹ данной схемой не допускается.

Статус: проект для выпуска рабочей КД. Монтаж — только квалифицированным персоналом.

				ЕМТН.19.01.02.59.00.000.0016 ЭЗ		Лит.	
Разраб.	МИТК-РК	22.07.26		Схема электрическая принципиальная стенда			
Пров.							
Т.контр.							
Н.контр.						Лист 1 Листов 1	
Утв.							
						Формат А3	