


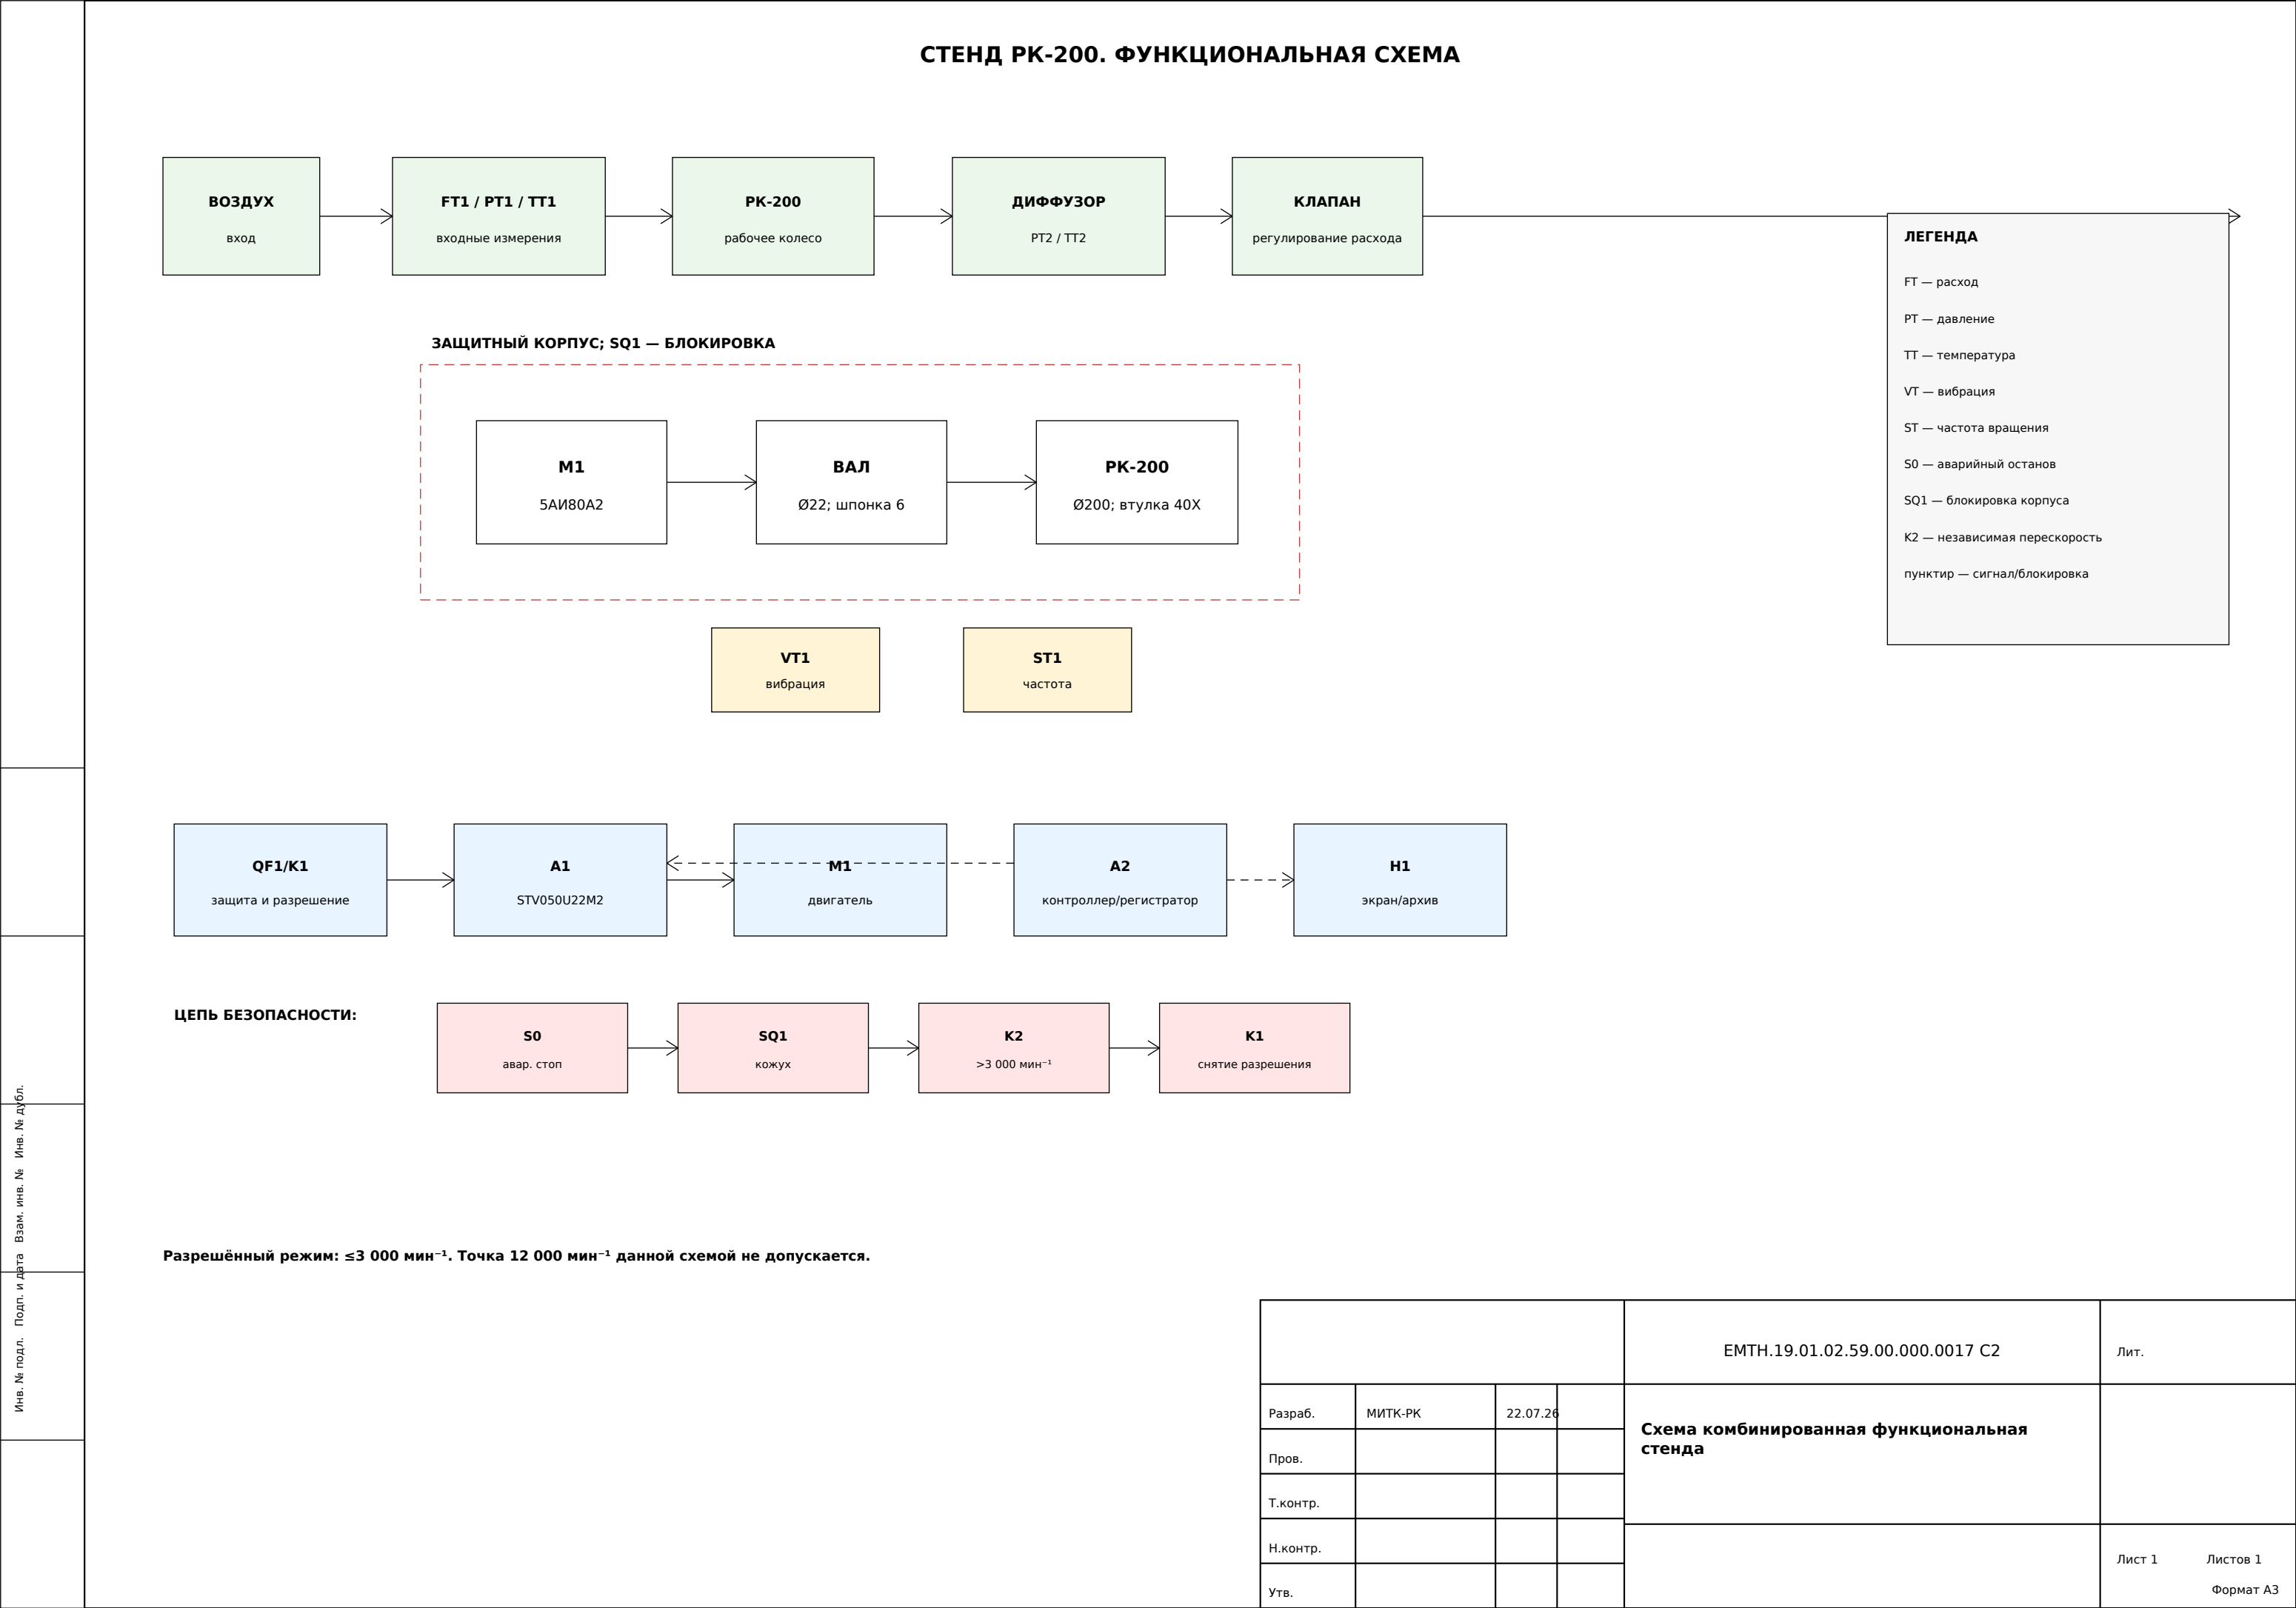

ЗАЩИТНЫЙ КОРПУС; SQ1 — БЛОКИРОВКА

M1

5AI80A2

ВАЛ

Ø22; шпонка 6

PK-200

Ø200; втулка 40X

VT1

вибрация

ST1

частота

QF1/K1

защита и разрешение

A1

STV050U22M2

M1

двигатель

A2

контроллер/регистратор

H1

экран/архив

ЦЕПЬ БЕЗОПАСНОСТИ:

S0

авар. стоп

SQ1

кожух

K2

>3 000 мин⁻¹

K1

снятие разрешения

Разрешённый режим: ≤3 000 мин⁻¹. Точка 12 000 мин⁻¹ данной схемой не допускается.

				EMTH.19.01.02.59.00.000.0017 C2		Лит.	
Разраб.	МИТК-РК	22.07.26		Схема комбинированная функциональная стенда			
Пров.							
Т.контр.							
Н.контр.						Лист 1	Листов 1
Утв.							

Формат А3